



CONCEPT, NOT FOR FABRICATION


REV	DESCRIPTION	DATE	BY
P1	Concept sheet	2026-09-25	AC

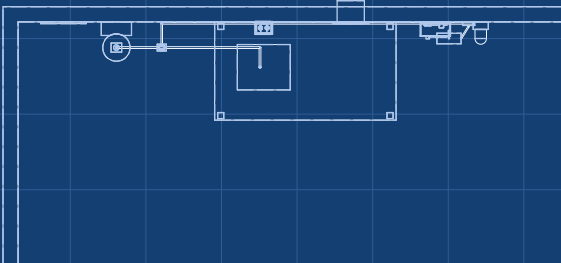


TOP VIEW
Scale 1:50

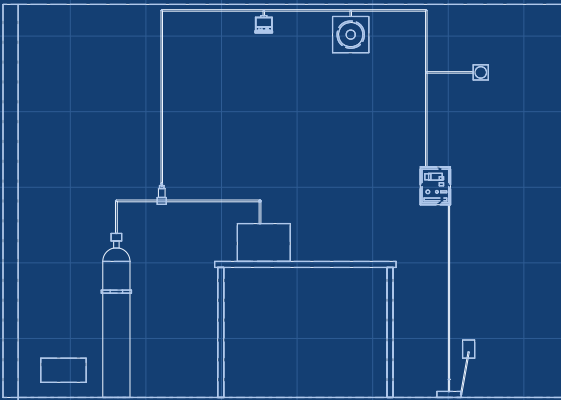

FRONT VIEW
Scale 1:50

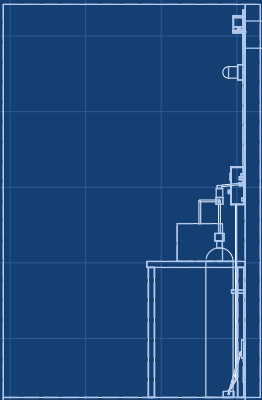

RIGHT VIEW
Scale 1:50

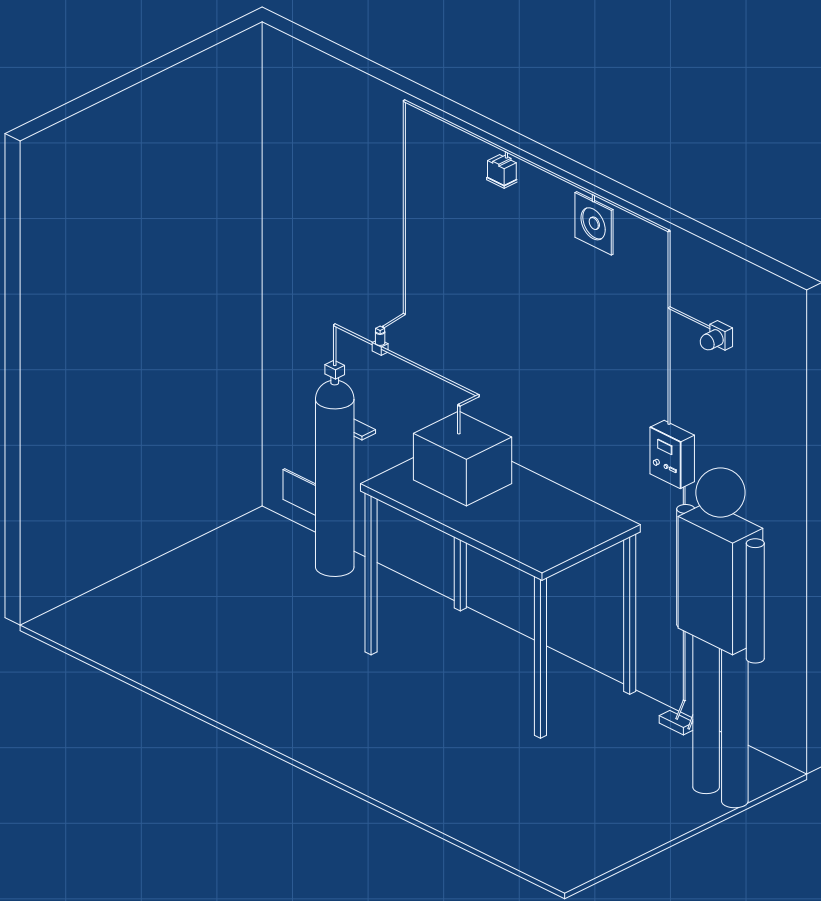

ISOMETRIC VIEW
Not to scale; figure is a 1.75 m person

KEY FIGURES

Warn at 10 % LFL (0.4 % vol H₂); trip at 25 % LFL (1.0 % vol)
Leak to valve closed about 35 s (estimate)
Exhaust 150 m³/h continuous, 300 m³/h boost (30 m³ room)
Fail-safe: NC valve closes on power loss, fault or fan failure
24 V DC build; mains only inside a certified supply
Parts about \$240 (indicative); budget \$180

H2GUARD

Leak detector and interlock concept

DRAWING NO. HGD-DWG-010			REV P1	SHEET 1 of 1	SIZE ANSI B
SCALE 1:50	UNITS mm	PROJECTION 	DATE 2026-09-25	DRAWN Amish Chadha	

MATERIAL / NOTES
Massing model for concept communication; room, bench and cylinder are context